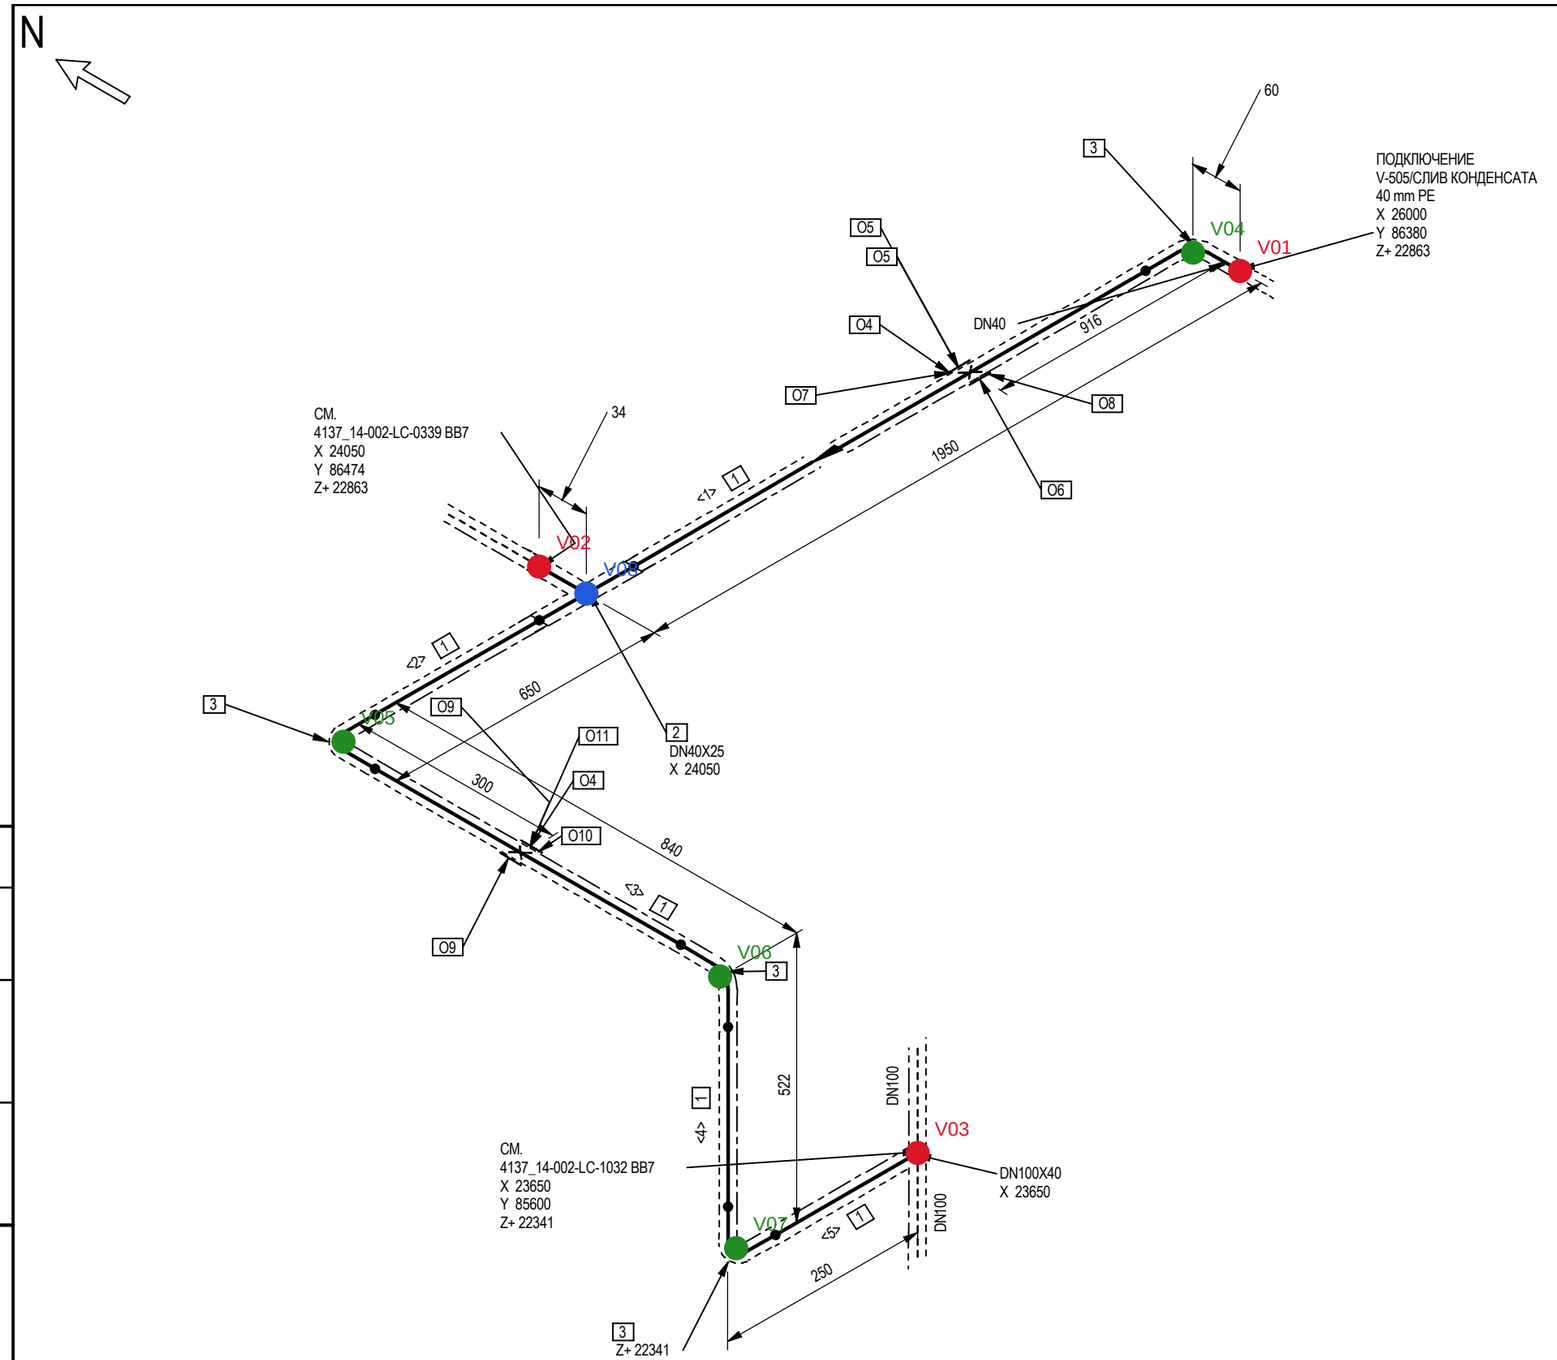


СПЕЦИФИКАЦИЯ МАТЕРИАЛОВ

№	Позиция	ItemCode	DN	Кол-во
1	ТРУБА 45Х4, Сталь 20, ГОСТ 32678-2014	PPR193	40	3.7 М
2	ТРОЙНИК 45Х32, 09Г2С, MNPZ-DCU-RD-4137.14-000-PI-TK-DDD-02.071	TEN109	40X25	1
3	ОТВОД П90 45Х4, СТАЛЬ 20, ГОСТ 17375-2001	E9R038	40	4
4	Опора 45-ТП-АС10, СТ3СП5, ОСТ 36-146-88	-	40	2
5	Лист 200Х200Х10, СТ3СП5, ГОСТ 19903-2015	-	40	2
6	Лист 200Х200Х12, СТ3СП5, ГОСТ 19903-2015	-	40	1
7	Опора Р-1000-А300-В350, MNPZ-DCU-RD-4137.14-000-PI-TK-DDD-03.535	-	40	1
8	Опора НО-D40-СТ3СП5-Р=2, MNPZ-DCU-RD-4137.14-000-PI-TK-DDD-03.222	-	40	1
9	Лист 351Х200Х10, СТ3СП5, ГОСТ 19903-2015	-	40	2
10	Опора Р-1000-А450-В300, MNPZ-DCU-RD-4137.14-000-PI-TK-DDD-03.535	-	40	1
11	Лист 351Х200Х12, СТ3СП5, ГОСТ 19903-2015	-	40	1

ДЛИНЫ ОТРЕЗКОВ

Поз. №	Длина, мм	DN	Поз. №	Длина, мм	DN	Поз. №	Длина, мм	DN
<1>	1862	40	<5>	141	40			
<2>	562	40						
<3>	720	40						
<4>	402	40						

Класс трубопровода	BB7	Группа и категория, класс опасности, группа горючести	B, IV, -, НГ							
Расчетные давление/температура, МПа/°С	0.53/204	Группа рабочей среды, категория (ТР ТС 032/2013)	2Ж, -							
Рабочие давление/температура, МПа/°С	0.53/195	Термообработка сварных швов	Нет	Изм.	Кол.уч.	Лист	№ док.	Подп.	Дата	
Оптимальное рабочее давление, МПа	0.01	Объем контроля сварных швов	1%	Разраб.						
Оптимальная рабочая температура, °С	103	Вид изоляции	НЕ	Проверил						
Способ испытаний	Гидр.	Тип обогрева	E5							
Вид испытаний	Пр.	Система АКЗ	8-С	Нач. отд.						
Давление испытаний, МПа	0.76	Дополнительные требования	-							

Стадия	Лист	Листов
Р	1	1

Номер линии	Номер чертежа
LC_1031	

Согласовано

Взам. инв. №

Подп. и дата

Инв. № подл.

Формат А3